




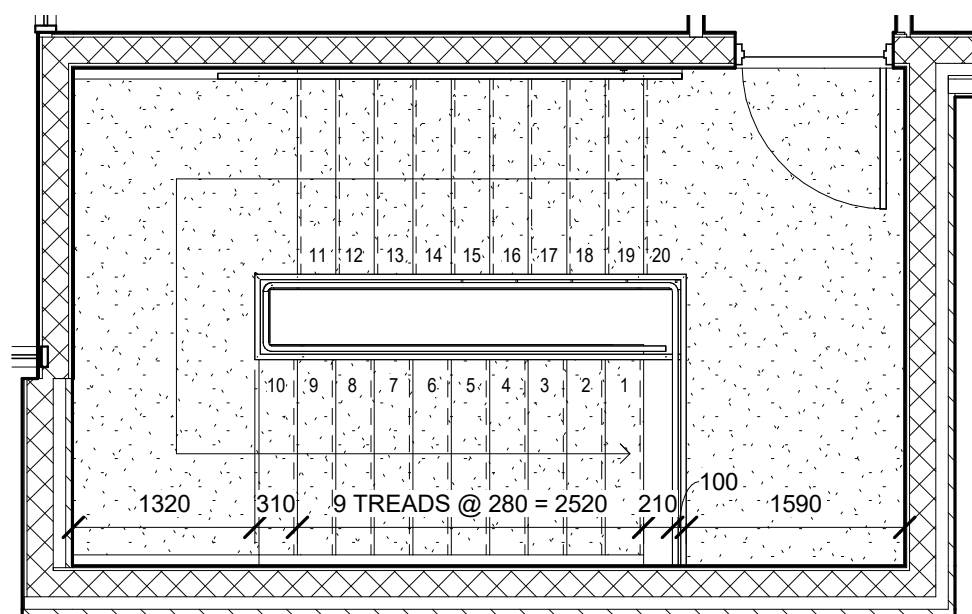


2 SECOND FLOOR PLAN
1:50
A-4

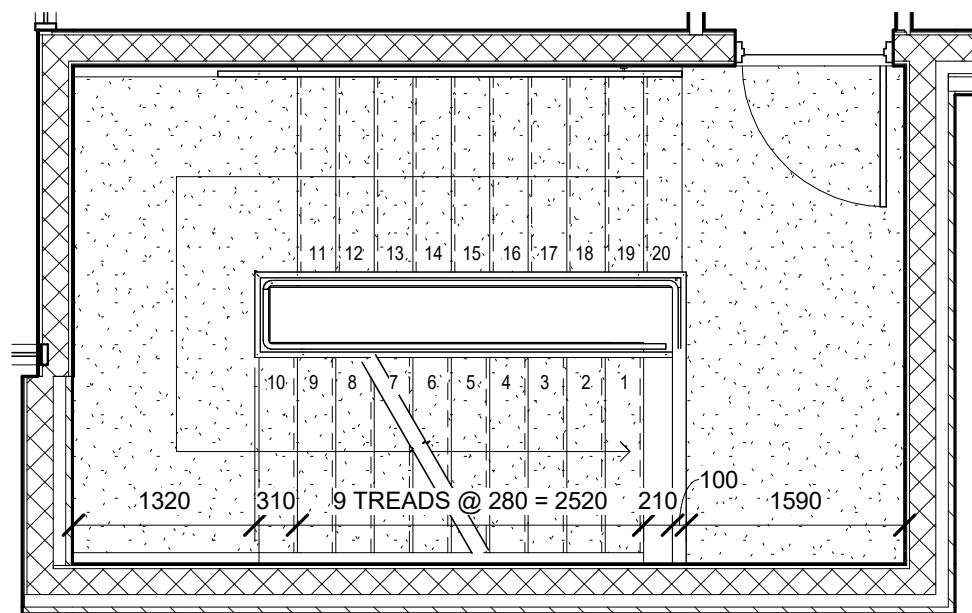

4 SECOND FLOOR PLAN
1:50
A-4

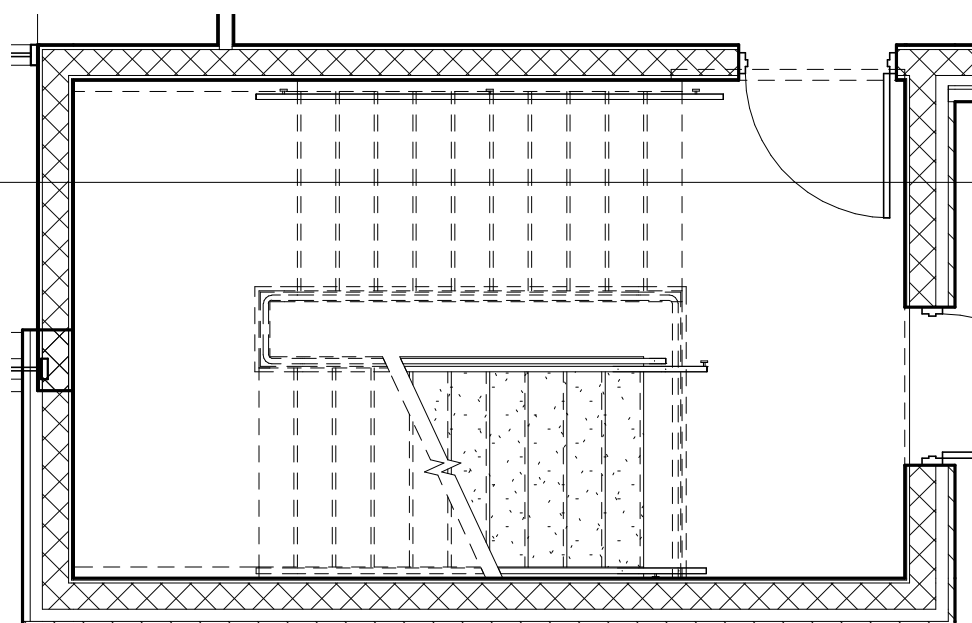

3 FIRST FLOOR PLAN
1:50
A-4

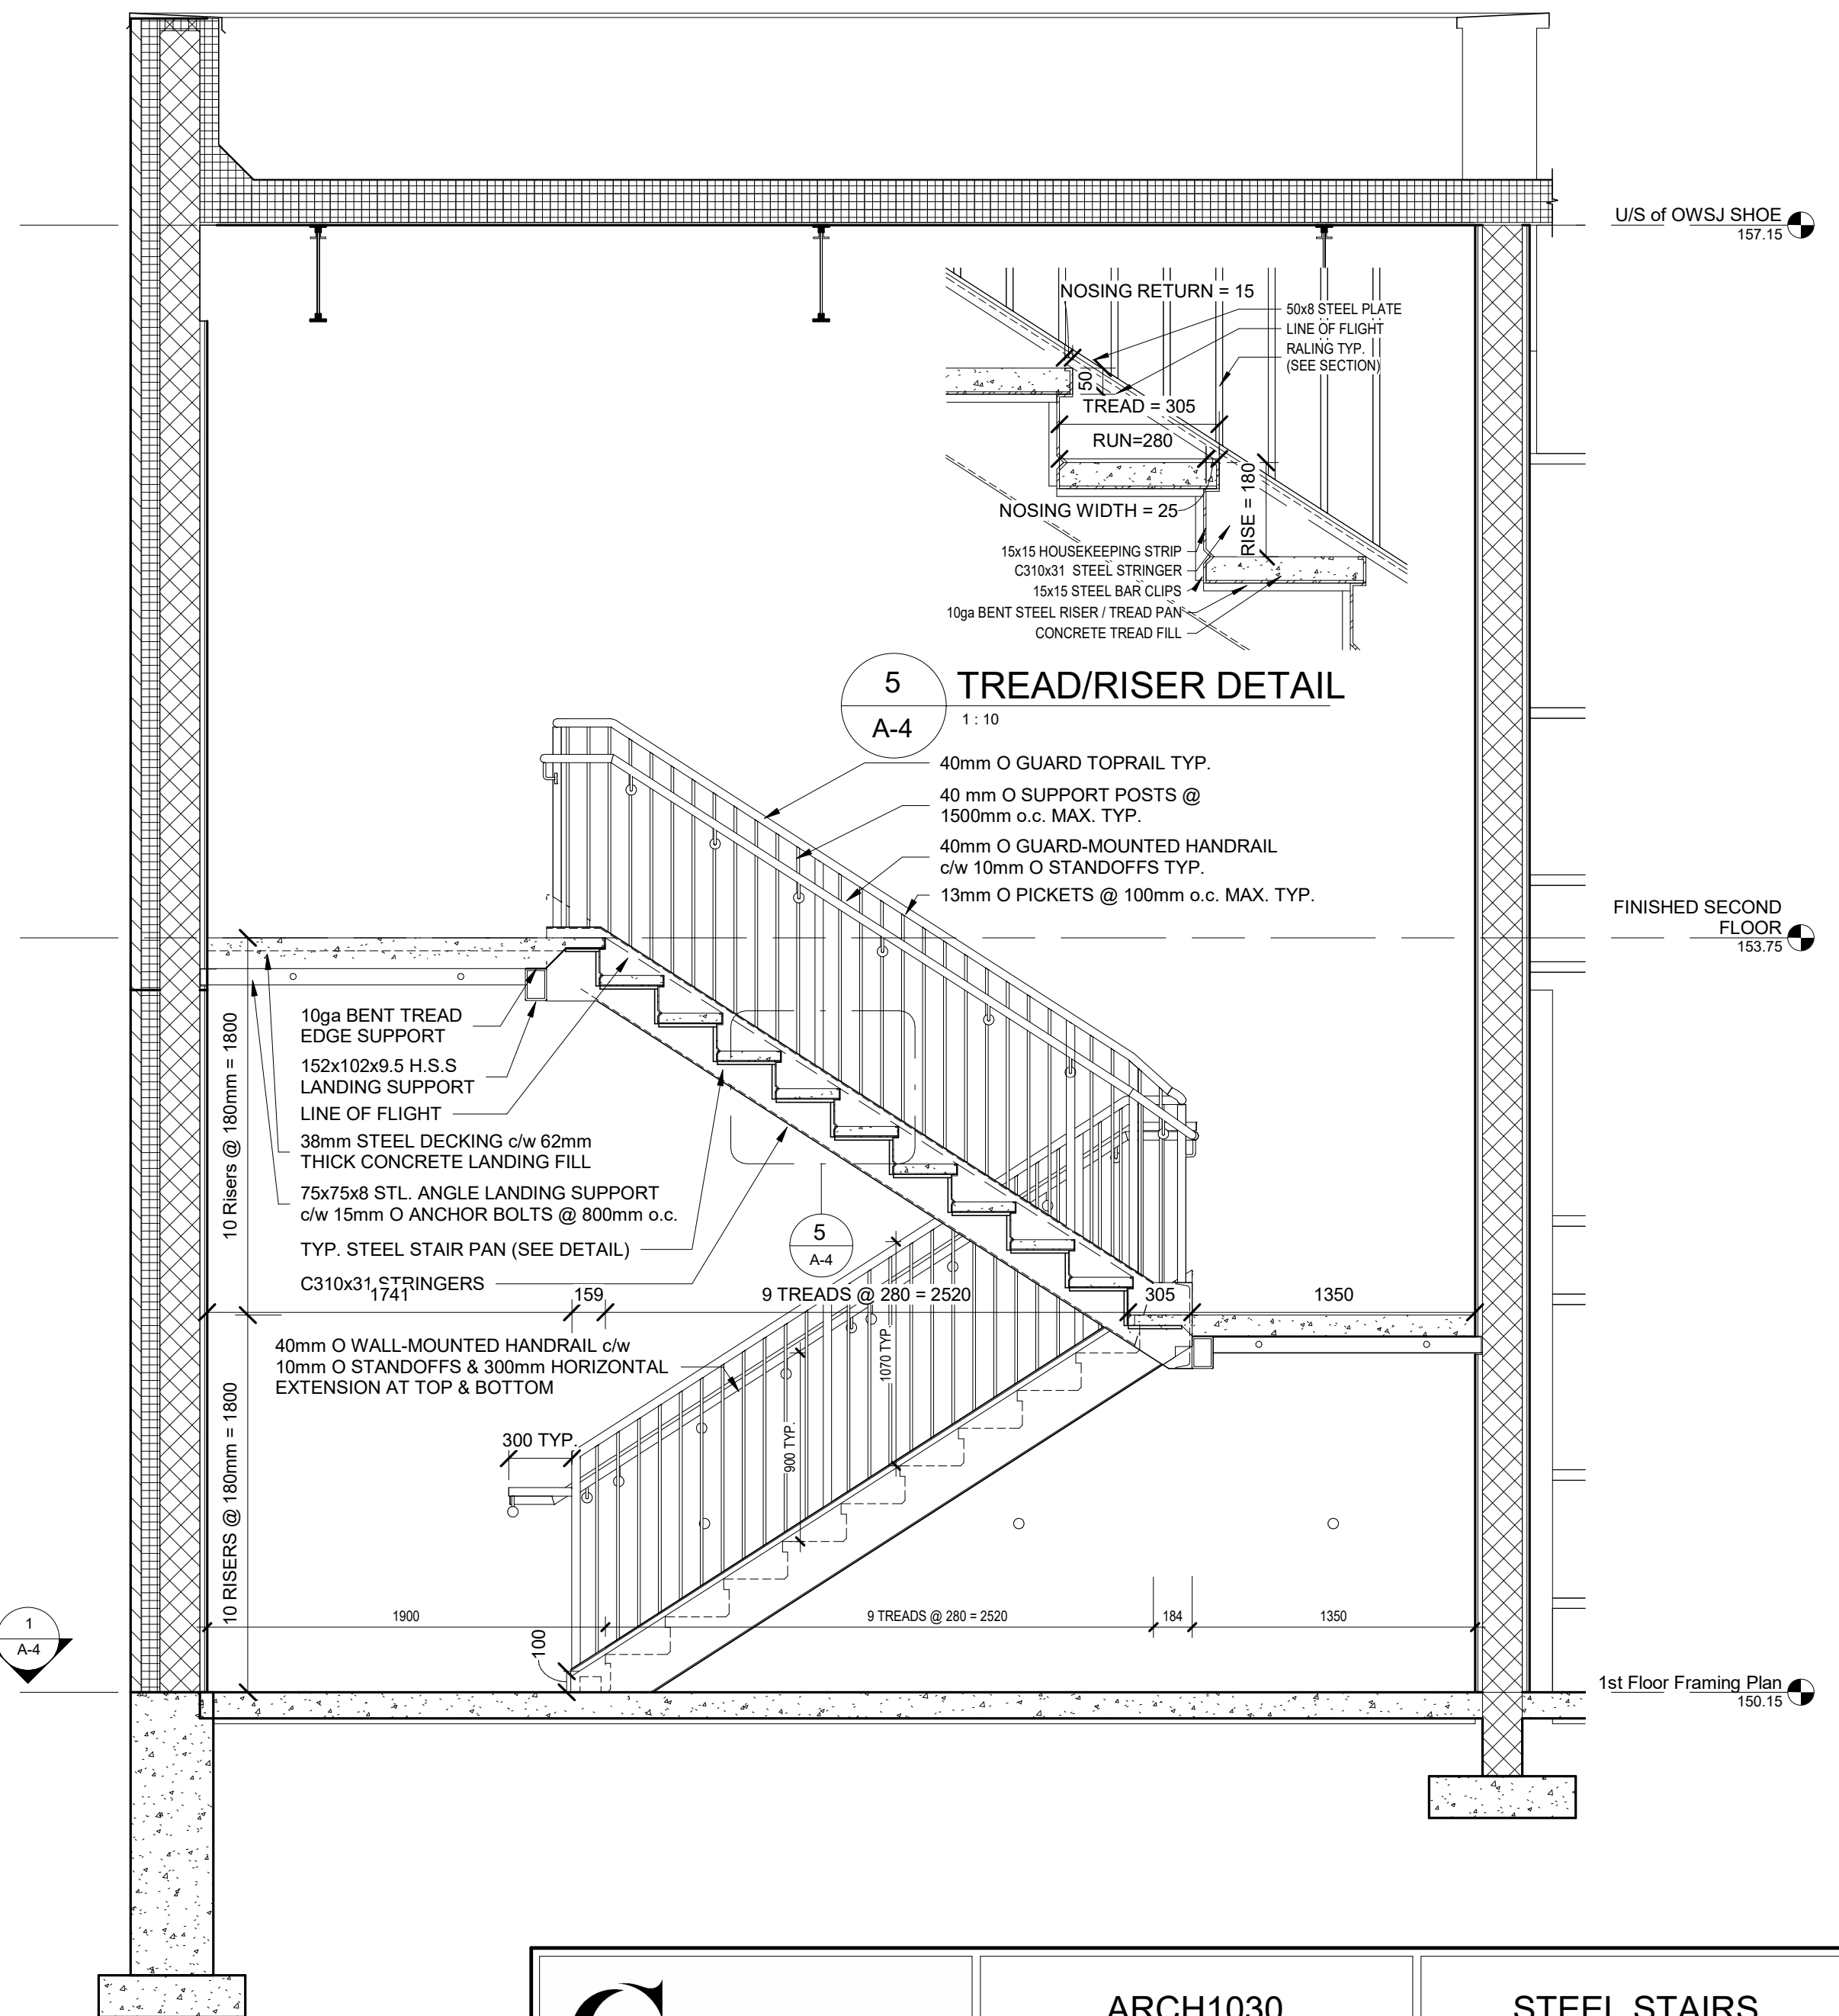

1 STAIR SECTION
1:25
A-4

5 TREAD/RISER DETAIL
1:10
A-4

 CONESTOGA Connect Life and Learning ARCHITECTURE - CONSTRUCTION ENGINEERING TECHNOLOGY	ARCH1030	STEEL STAIRS	
	J.D. GERRARD	Date NOV.23.2020	Sheet No. A-4
		Drawn by K. DICK	Scale As indicated

2020-12-03 2:22:33 AM